简约有度，归家有院。

V7 / 客户方案更新 · 现代中式 · 两层主体 + 可使用屋顶

12 × 11 m

主体建设控制范围

前后院在范围之外

四间卧室

三间卫生间

约31m²主卧套房

一层方便长者起居；

二层保留两间客卧；


屋顶喝茶、活动与少量洗晒。

本次同步：室内方案、九宫布局研读、Blender模型与客户圈点网页。



先把边界说清楚

12×11米为用户确认的主体建设范围；四角坐标、绝对高程与完成面厚度仍需现场复核。

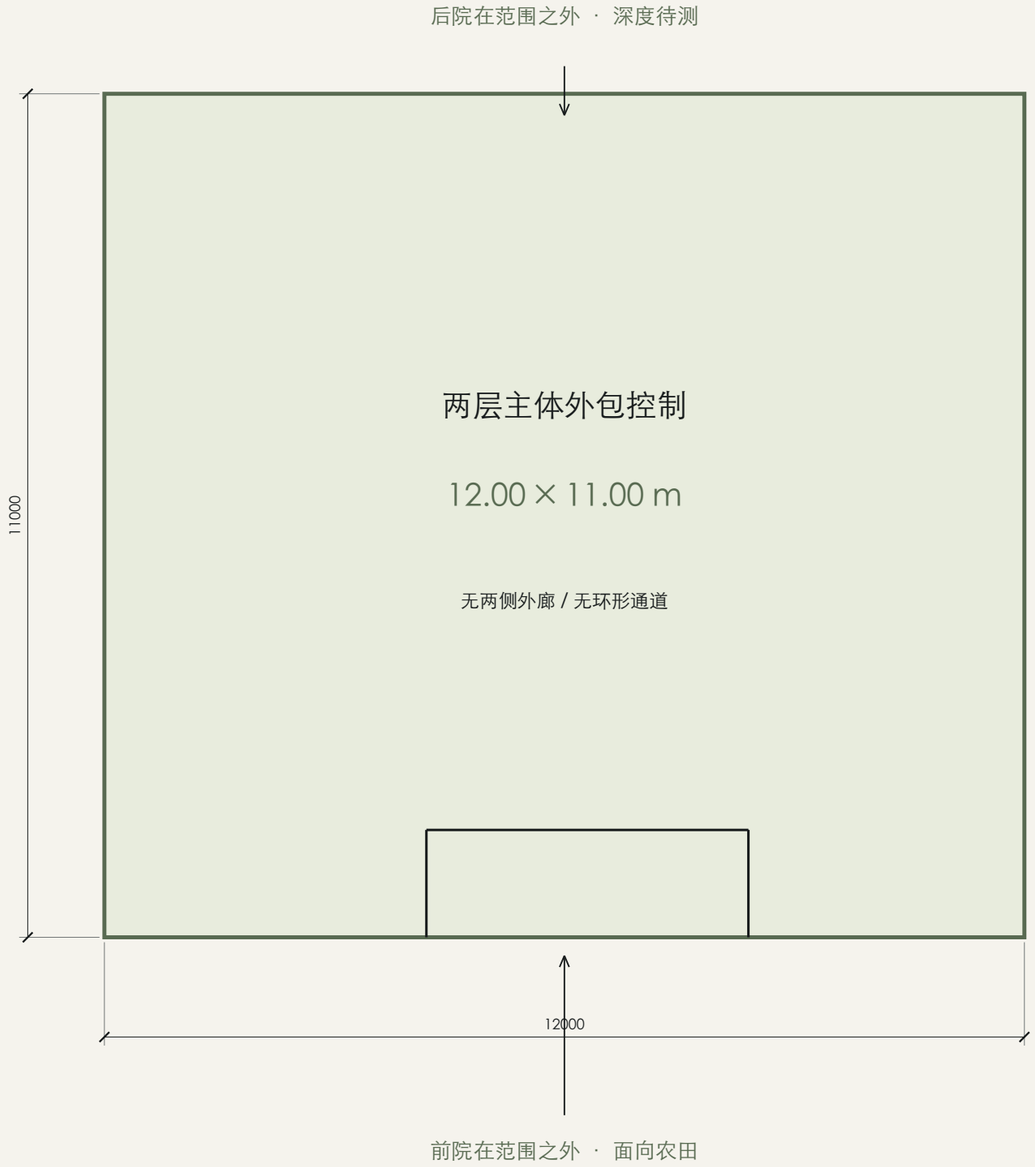

132m² 是控制矩形面积

不能直接把两层相乘当作核定建筑面积；门廊、阳台、楼梯出口等需按适用计算口径复核。

图纸、模型与效果图的分工

平面与Blender模型采用同一建筑几何；ImageGen表达材料和光影，不能从图像像素反推尺寸。院深、邻房与远景不是测绘成果。

本次实际改动


二层后排组成约31m²主卧套房；原湿区与走道重排为套卫 + 公卫；一层保留公卫并集中洗衣。主体外包、楼梯与外门窗位置保持。

饰面控制

米白墙面、浅木柜体、浅灰地面和深灰细框。侧墙不预设外窗，不以假设侧院解决采光或通行。

一层：回家、团聚与长者起居

建筑平面 1:60 / A3原尺寸打印 · 尺寸mm；净面按当前图示墙面计算。

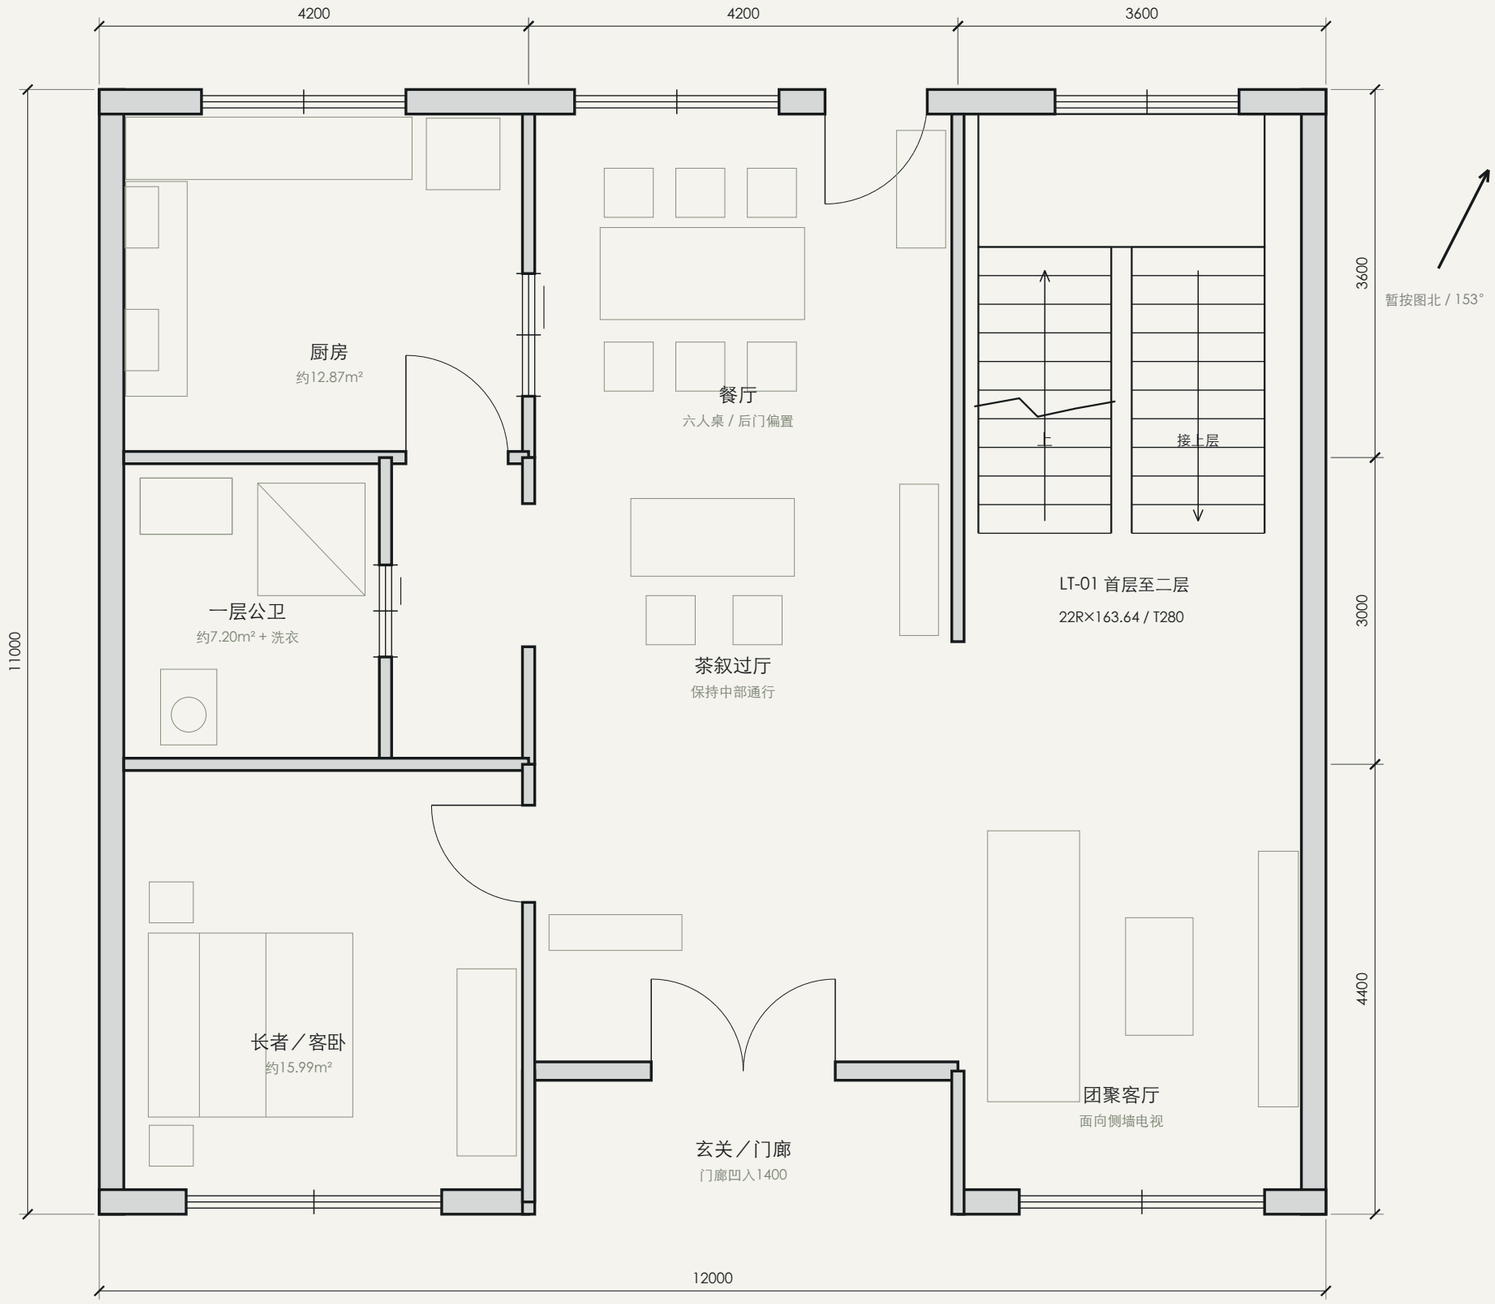

公私分开

长者／客卧留在一层。卫生间从过道进入，不需要穿越卧室。厨房、餐厅与后院联系，入户与后门错位。

客厅与茶厅

客厅电视设在实体侧墙，前窗保留采光。茶厅适合临时聚会，桌椅不占用前后主通路。

洗衣与卫浴

公卫图示净面约7.20m²，保留淋浴分隔，并将洗衣移到干区。排风、排水和电位保护待专业深化。


图示层高：3.60m

入户门洞：1800mm

门廊凹入：1400mm

二层：主卧套房与两间客卧

建筑平面 1:60 / A3原尺寸打印 · 尺寸mm；净面按当前图示墙面计算。

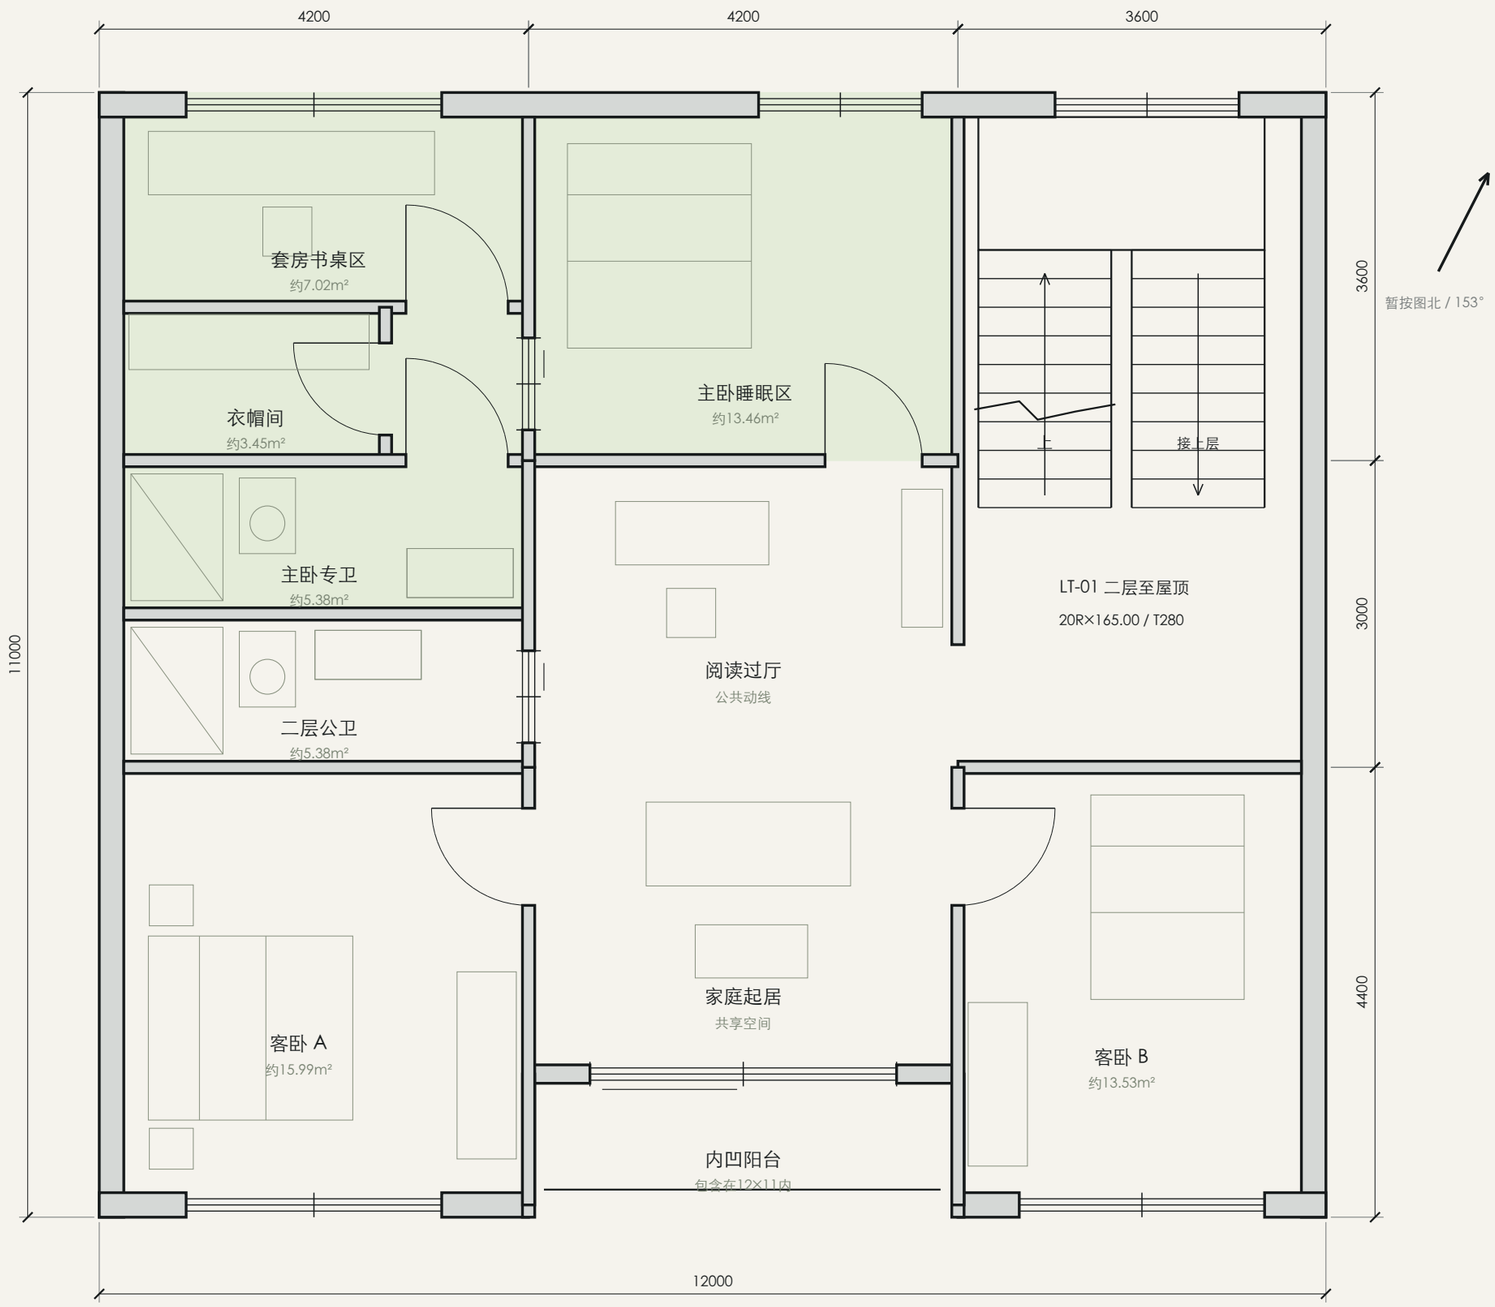

主卧套房

约31m²套内空间

后排主卧经D10连接衣帽、书桌与专卫。绿色为套房范围，公共走道不穿入套房。

二层两处卫浴

专卫从套内过道进入。公卫从公共阅读过厅经D09进入；两处湿区独立分隔。

客房与家庭起居

前侧两间客房分别约15.99m²和13.53m²。中央起居联系内凹阳台，阳台不扩大主体外包。

图示层高：3.30m


后排套房与公共过厅设门分隔。

面积未扣局部管井／饰面。

主卧套房：睡眠、阅读、更衣、洗浴

方案净面合计约31.1m²；套房通过公共过厅的一处主入口进入。

套房局部平面 / 1:40

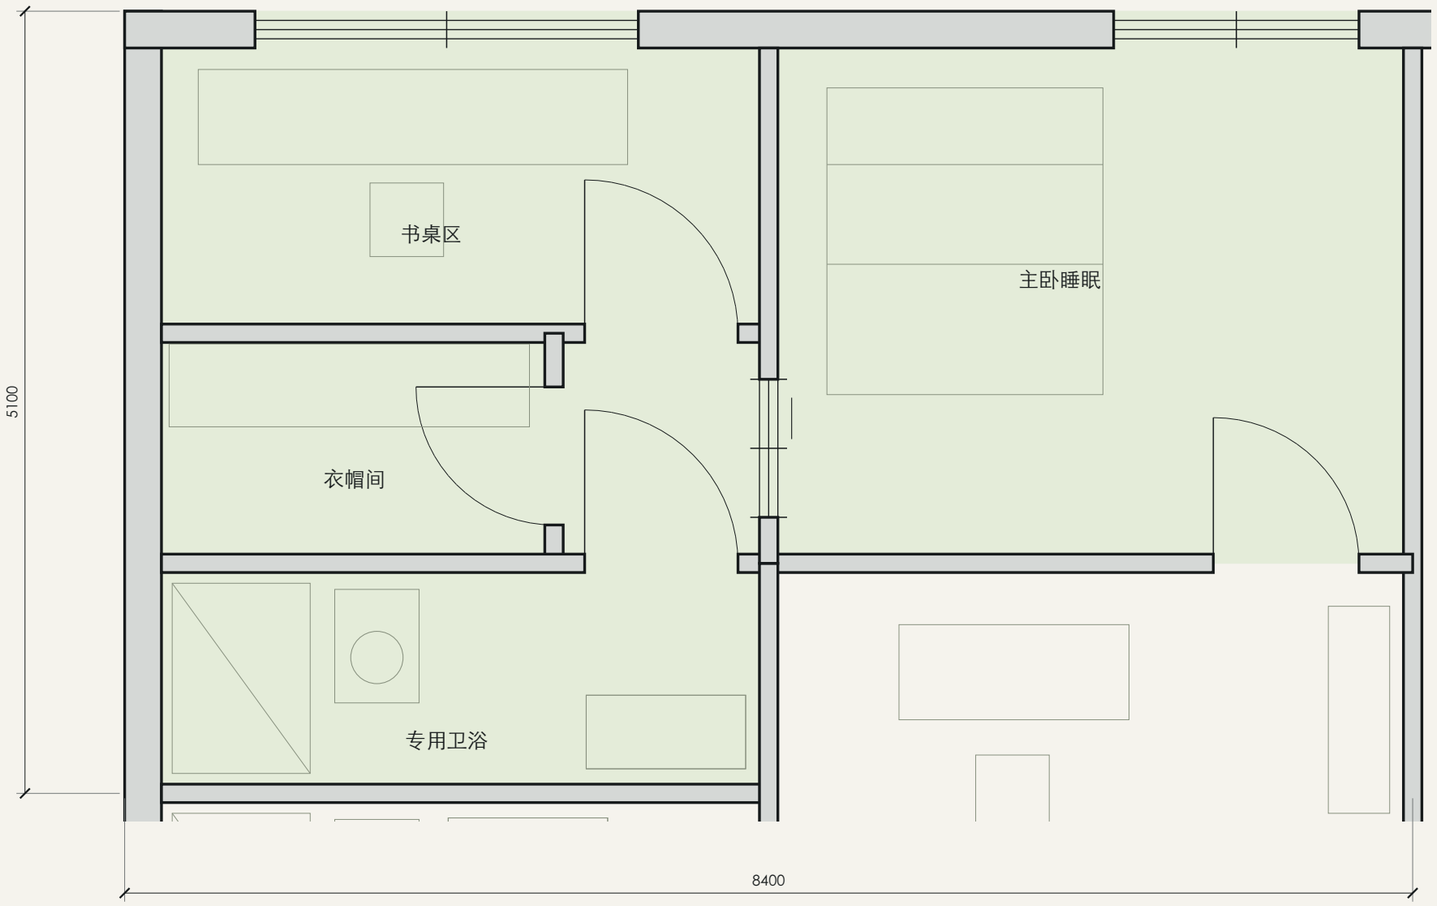

分区	图示净面
主卧睡眠区	13.46m²
书桌区	7.02m²
衣帽区	3.45m²
套内通道	约1.77m²
专用卫浴	5.38m²
合计	约31.1m²

门位与床位

D10为睡眠区与套内通道之间的900mm门洞；床头靠实体后墙，避开右侧后窗。卫生间门位于套内通道，避免正对床。


衣帽区保持可用

采用单侧540mm深柜，图示余下站立通道约840mm。柜门、把手与现场完成面一起复核。

三卫：私密、通行与维护一起考虑

一层公卫约7.20m²；二层公卫和套卫各约5.38m²。尺寸为建筑方案，不是卫浴设备加工图。

二层卫浴局部 / 1:30

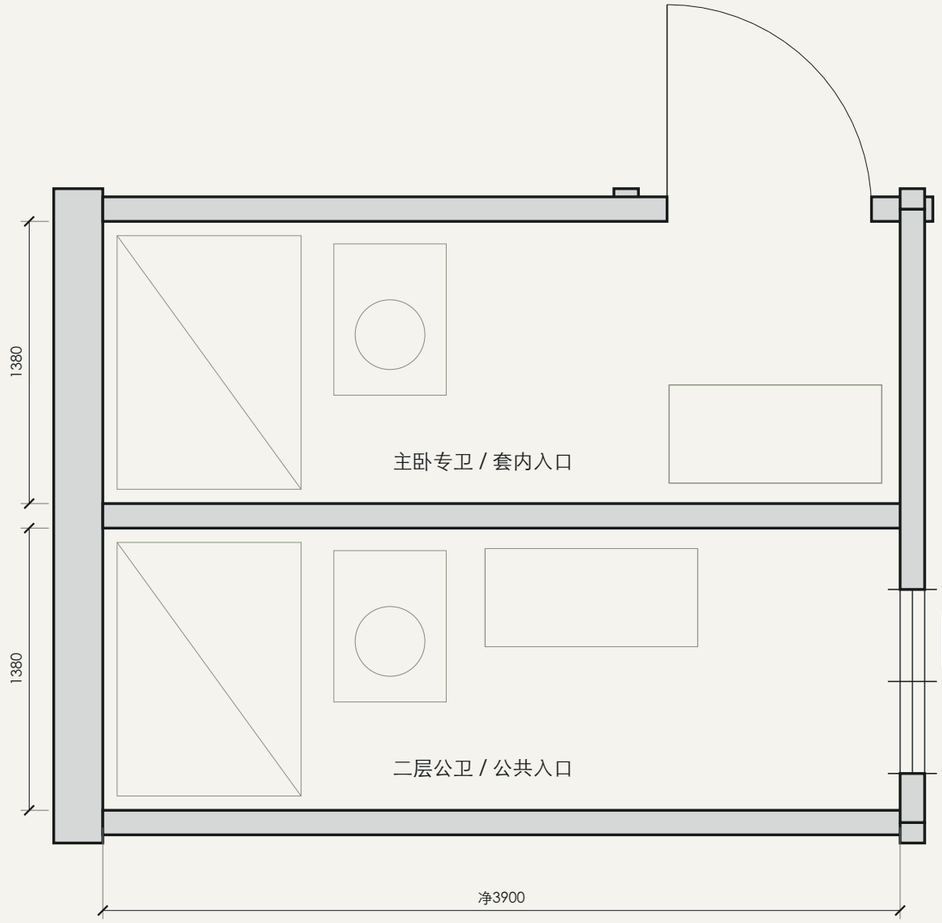

台盆避让入口，坐便与淋浴沿长边组织。
两卫分隔墙暂120mm，管井与通风井再深化。

入口分别组织

主卧专卫从北侧套内通道进入；公卫从东侧公共过厅进入。两处门洞各有独立动线，不互相借道。

湿区尽量叠置

新增二层卫生间占用原卫浴及原过道范围；没有放到一层卧室、厨房或餐厅上方。排水支管与检修口集中复核。

长条卫浴的取舍

每间净深约1380mm，属于紧凑型。采用短进深台盆、分隔淋浴和移门；设备选型后须再校核门口与坐便前净距。

一层留更宽裕的使用面

长者主要使用一层公卫；淋浴分区、扶手基层、夜间照明与防滑一起深化。洗衣机旁预留检修，湿区用电按专业图落实。

施工接口

楼板降板／找平、防水上翻、排水坡向、独立排风、管井防火与隔声均需专业施工图补齐。当前不以效果图替代这些节点。

客厅与玄关：留白，比装饰更有力量

室内效果用于材料、配色与家具意向；门窗定位和尺寸以本版平面及模型为准。



团聚客厅

浅色沙发、矮柜与小茶几，电视位于实体侧墙；前窗保持完整采光。



入户玄关

鞋柜与轻格栅安排在动线旁，不用满墙造型，也不把入口围成狭窄通道。

厨房与餐厅：节日团聚，也要好打理

室内效果用于材料、配色与家具意向；门窗定位和尺寸以本版平面及模型为准。



L形封闭厨房

平整柜门、浅色台面和可擦洗墙面。灶台与水槽分开，排油烟另做管路。



六人餐厅

日常六人桌；需要临时加座时使用中部共享区，后门前保留通行。

主卧套房：安静、独立、日常可用

室内效果用于材料、配色与家具意向；门窗定位和尺寸以本版平面及模型为准。



后排主卧

1.8米床靠实体后墙，窗在右侧；专卫通过衣帽通道到达。



套房书桌区

书桌沿后窗布置，既能短时工作，也能独处阅读；属于套房私密区域。

套房收纳与专卫：紧凑空间有明确分工

室内效果用于材料、配色与家具意向；门窗定位和尺寸以本版平面及模型为准。



衣帽区

单侧柜体，避免用岛台或双排高柜挤占站立空间。



主卧专卫

本图为材质意向；长条卫浴入口、台盆、坐便和淋浴以C-06及3D位置为准。

客卧：长者与返乡家人都能住得方便

室内效果用于材料、配色与家具意向；门窗定位和尺寸以本版平面及模型为准。



一层长者／客卧

床头移离卫生间隔墙，柜体平整，保留床边与进门通行；二层客卧A为同型房。



二层客卧 B

1.5米床，简单床头与衣柜；减少积灰装饰，方便短住后的清洁和封存。

共享起居与公卫：家人有相聚，也有界限

室内效果用于材料、配色与家具意向；门窗定位和尺寸以本版平面及模型为准。



家庭起居 + 内凹阳台

阳台在主体内凹，保留通透的前侧视线；不增加两侧外廊。




二层公卫

只从公共过厅进入，供两间客卧和公共活动使用；与主卧专卫分开。

屋顶：喝茶、活动、少量洗晒

平屋顶的使用保留在12×11米范围内；廊架为开放遮阴构架，非封闭第三层。

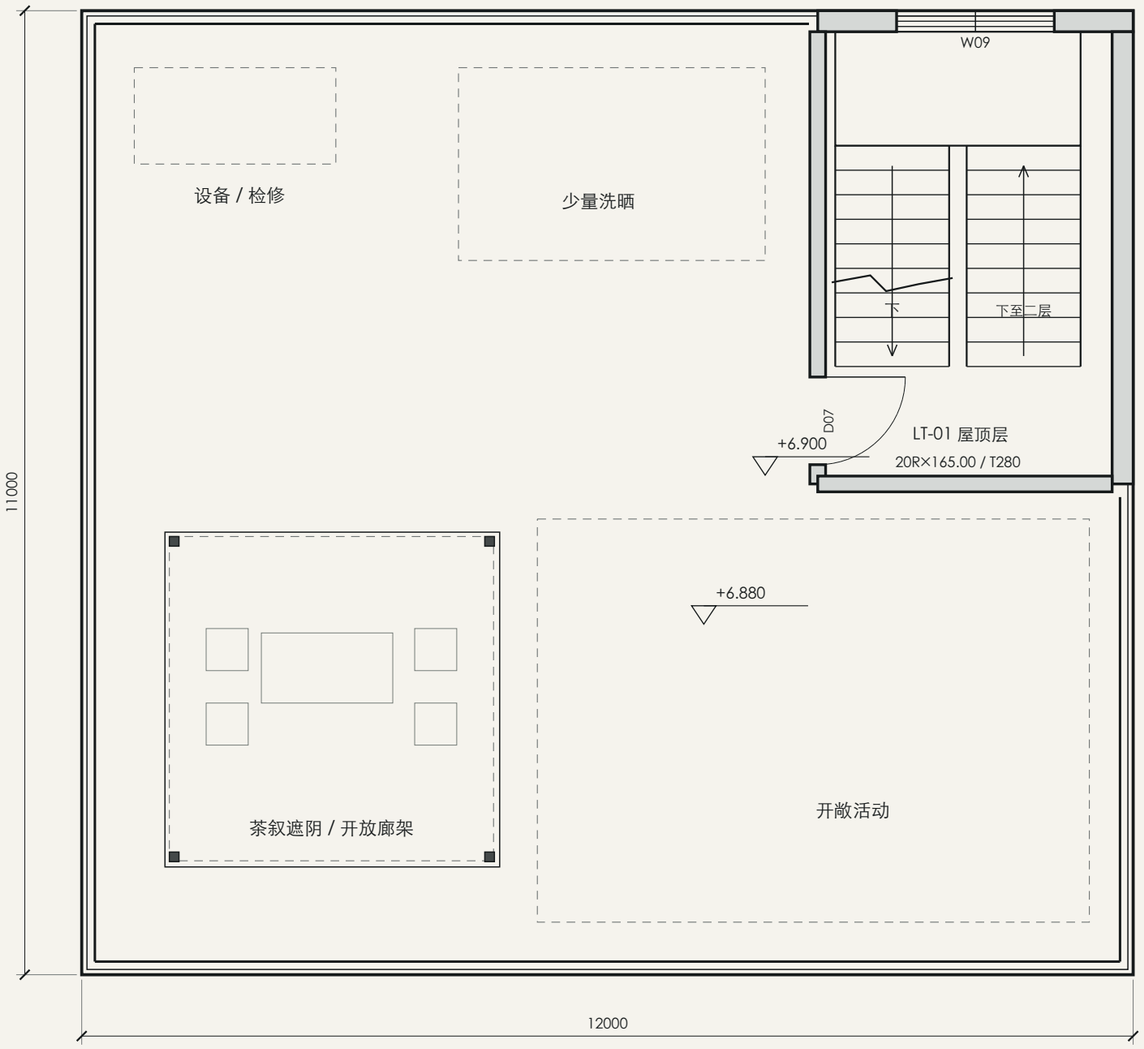



前侧茶棚约3.7×3.7米，中央留开敞活动面；后侧只放少量洗晒与设备。花箱、家具不得妨碍楼梯出口和检修。


屋面防水、主排水与溢流、栏杆和廊架连接由专业深化。

同一套数据，核对内外空间关系

下列为Blender尺寸模型渲染；模型与本册平面使用同一版本。




一层模型 / 家具与生活动线

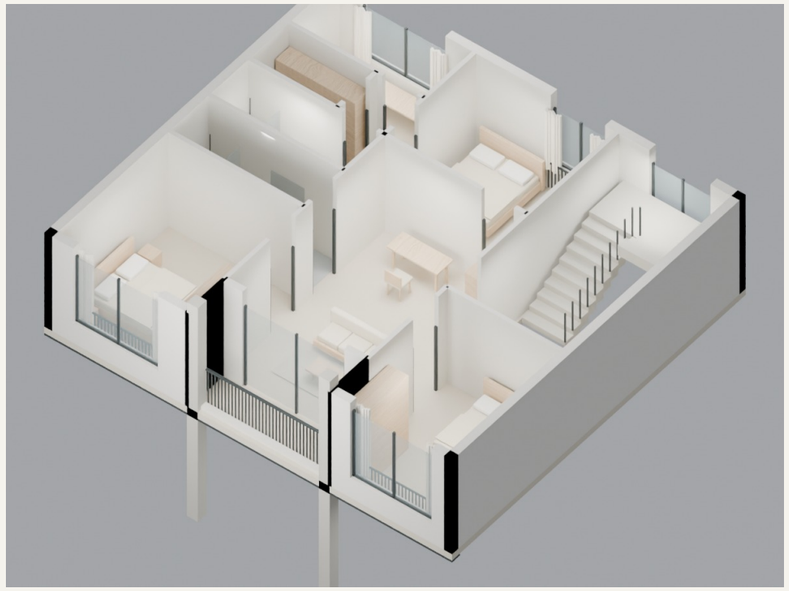

二层模型 / 主卧套房与两间客卧



主体外观 / 不增加环绕过道

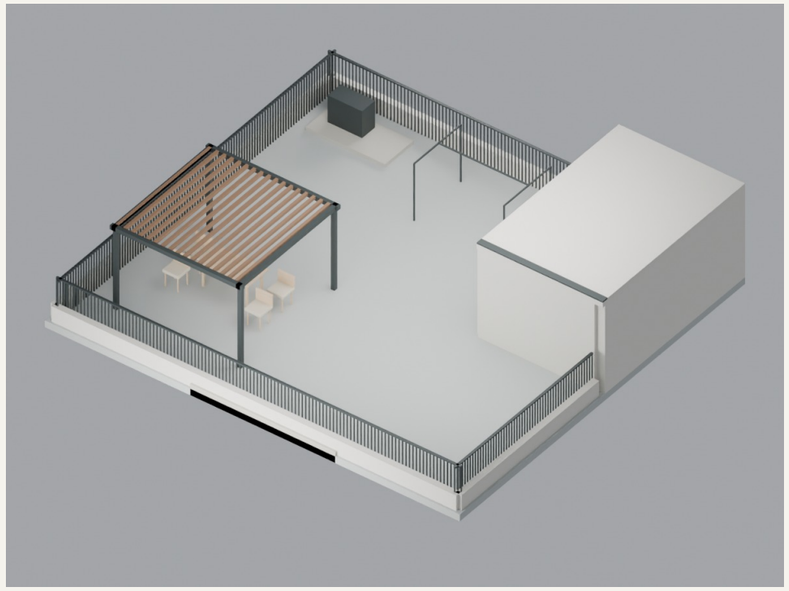

屋顶模型 / 茶棚与楼梯出口

九运亥山巳向：一页室内布局建议

条件盘：九运建成使用、建筑朝向约153°、采用下卦；数值为山星 / 向星，不是流年盘。

按宅向九宫格分区 / 图上方为后院

正西 8 / 1 厨房／书桌衣帽	西北 9 / 9 餐厅／主卧睡眠	正北 5 / 4 后部楼梯
西南 4 / 5 公卫／套卫湿区	中宫 1 / 8 茶叙／阅读过厅	东北 7 / 2 楼梯前厅
正南 6 / 3 前左客卧	东南 2 / 7 正门／内凹阳台	正东 3 / 6 客厅／前右客卧

前院／农田 · 巳向约153°

方法：宅向九宫格，供整体功能讨论，非逐点罗盘定穴。地图真北与罗盘磁北需统一；实测跨山界或涉及兼向替星时须重排。

主卧

后中格为西北9/9，按传统为双星到坐；因此将原后排主卧连成套房。仍先校核采光、隔声、通风与私密动线。

厨房

主体落西宫8/1，并非图纸左上就是西北。保留L形台面；水槽与灶台不紧贴，灶不正对入户，排油烟独立。

厕所

湿区以西南4/5为主，专卫从套内进入、公卫从过厅进入。维持干燥、洁净和排风，不因数字把厕所移到卧室或厨房上方。

客卧与中宫

前左客卧为南宫6/3，前右为东宫3/6；用安静配色、实体床头与清晰门位。中宫1/8保留通行，不堆高柜或设置水池。

正门与院落

前中为东南2/7，入口与后门错位，院落保持清爽。未据星数增设水景、镜阵或重型摆件。

从客户意见，走到同一套修订图

本册是客户方案与建筑尺寸复核稿；V5旧二层与湿区图已被本版方案变更，不能混用开工。

在线圈点提建议

打开网页，按楼层选区域，拖动画圈或点选位置，填写文字后保存。可导出带圈点图片、意见JSON，或复制含意见的链接发给设计方。意见默认只保存在浏览器。

空置期间容易维护

平整柜门、少量木色、简单灯具。水电按使用区域分组；临走能关闭非必要供水和设备，排水地漏与通风做好维护。屋顶不做积水景观和重型种植。

交付给专业设计与施工方

以本版12×11米外包、套房门位、卫浴重排、家具与设备需求为输入，补齐现场测绘、结构／基础、抗震、给排水、电气、暖通及完整节点。江苏平原也不等于可以省略抗震复核。

图像与依据

ImageGen为材质和空间意向；Blender与矢量平面核对几何。飞星表参考Joey Yap《Period 6-9 Flying Star Charts》九运SE2/SE3向；格宫法参考《Real Feng Shui》平面叠宫说明。风水属文化安排，不保证健康或财运。

在线查看与圈点

手机扫码，或点击下方链接：
完整3D / 分区效果 / 圈点意见

lgch3136.github.io/courtyard-house

飞星参考表（作者公开资料）

宅向九宫格方法参考

最终施工：以专业复核并签发的
完整施工图为准。